


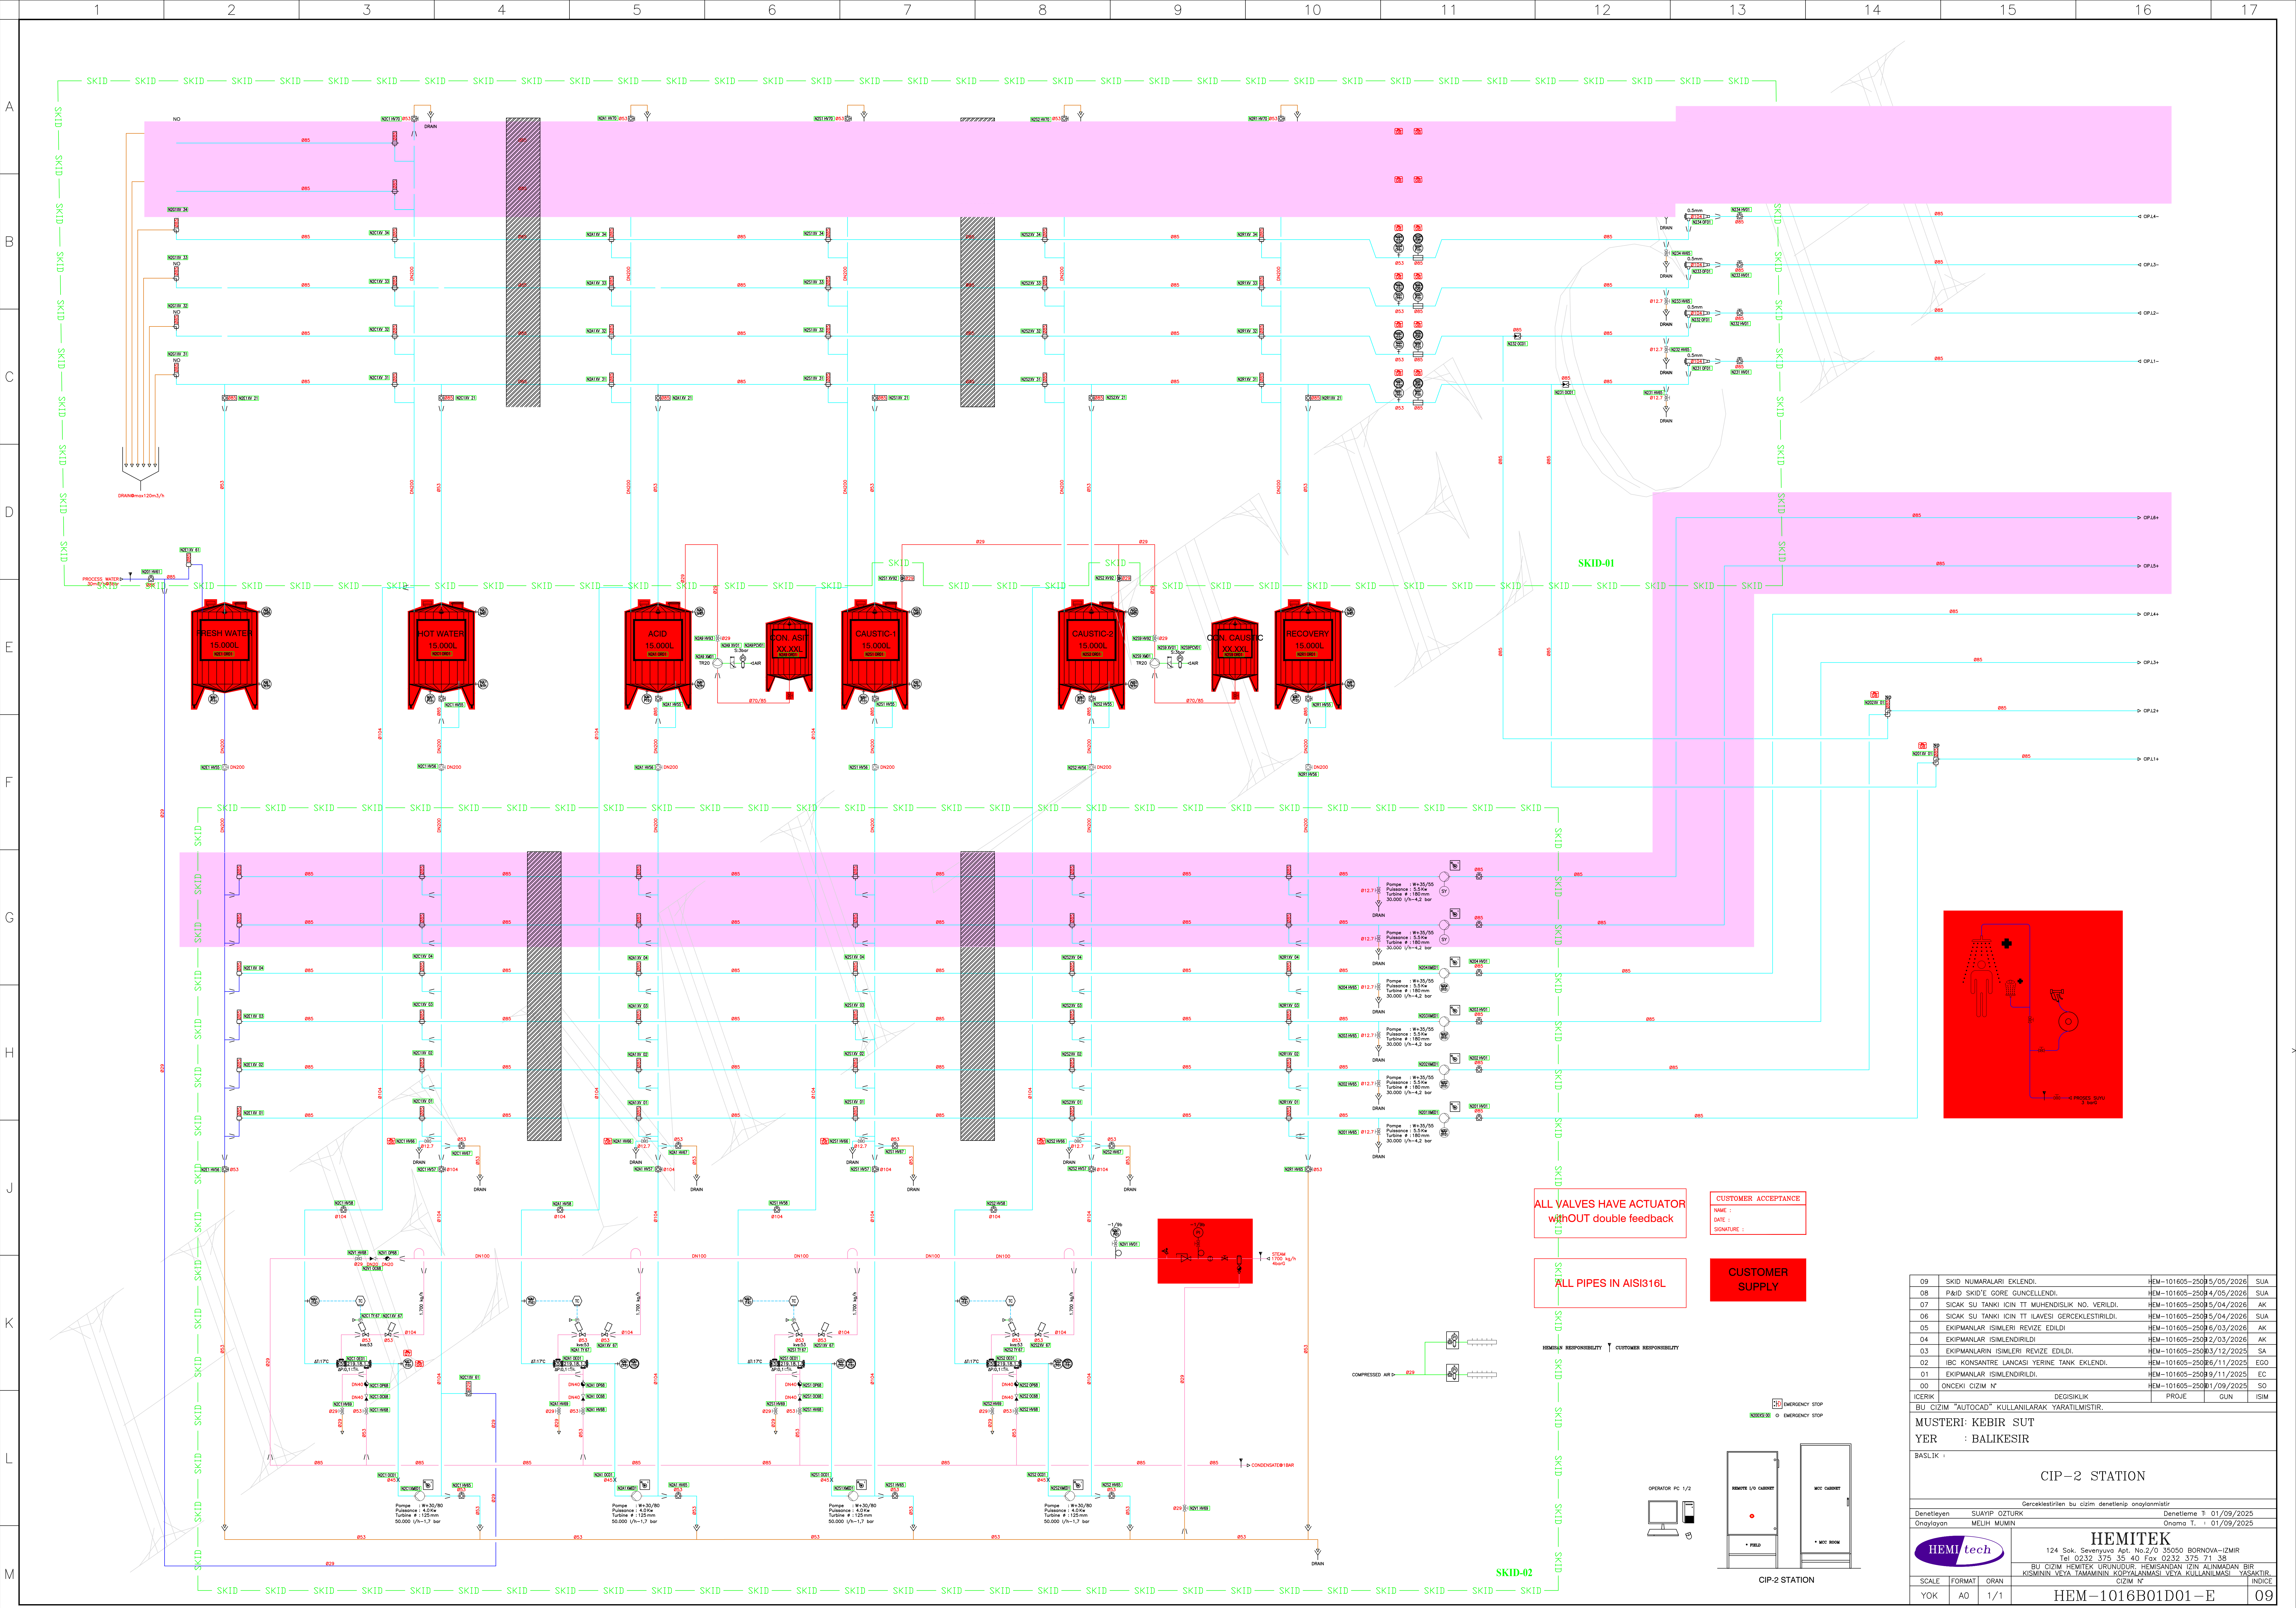

09	SKID NUMARALARI EKLENDİ.	HEM-101605-2500	5/05/2026	SUA
08	PAİD SKİD'E GÖRE GÜNCELLENDİ.	HEM-101605-2500	4/05/2026	AK
07	SICAK SU TANKI İÇİN TT MUHENDİSLİK NO. VERİLDİ.	HEM-101605-2500	5/04/2026	AK
06	SICAK SU TANKI İÇİN TT İLAVESİ GERÇEKLEŞTİRİLDİ.	HEM-101605-2500	5/04/2026	SA
05	EKİPMANLAR İSİMLERİ REVİZE EDİLDİ	HEM-101605-2500	6/03/2026	AK
04	EKİPMANLARIN İSİMLERİ REVİZE EDİLDİ	HEM-101605-2500	2/03/2026	AK
03	EKİPMANLARIN İSİMLERİ REVİZE EDİLDİ.	HEM-101605-2500	3/12/2025	SA
02	IBC KONSANTRE LANCASI YERİNE TANK EKLENDİ.	HEM-101605-2500	6/11/2025	EGO
01	EKİPMANLAR İSİMLENDİRİLDİ.	HEM-101605-2500	9/11/2025	EC
00	ÖNCEKİ ÇİZİM N°	HEM-101605-2500	1/09/2025	SO
İÇERİK	DEĞİŞİKLİK	PROJE	GÜN	İSİM
BU ÇİZİM "AUTOCAD" KULLANILARAK YARATILMIŞTIR.				
MÜSTERİ: KEBİR SUT				
YER : BALIKESİR				
BASLIK :				
CIP-2 STATION				
Denetleyen: SUAMP ÖZTÜRK				
Onaylayan: MELİH MUMİN				
Denetleme Tarih: 01/09/2025				
Onaylama Tarih: 01/09/2025				
		HEMITEK 124 Sok. Sahyaywa Apt. No:2/0 35060 BORNOVA-İZMİR Tel: 0232 375 35 40 Fax: 0232 375 71 38 BU ÇİZİM HEMİTEK ÜRÜNÜDÜR. HEMİSANDAN İZİN ALINMADAN BİR KİŞİNİN VEYA TİMMİNİN KOPYALANMASI VEYA KULLANILMASI YASAKTIR. CİZİM N°		
SCALE	FORMAT	ORAN		
YOK	A0	1/1	HEM-1016B01D01-E 09	