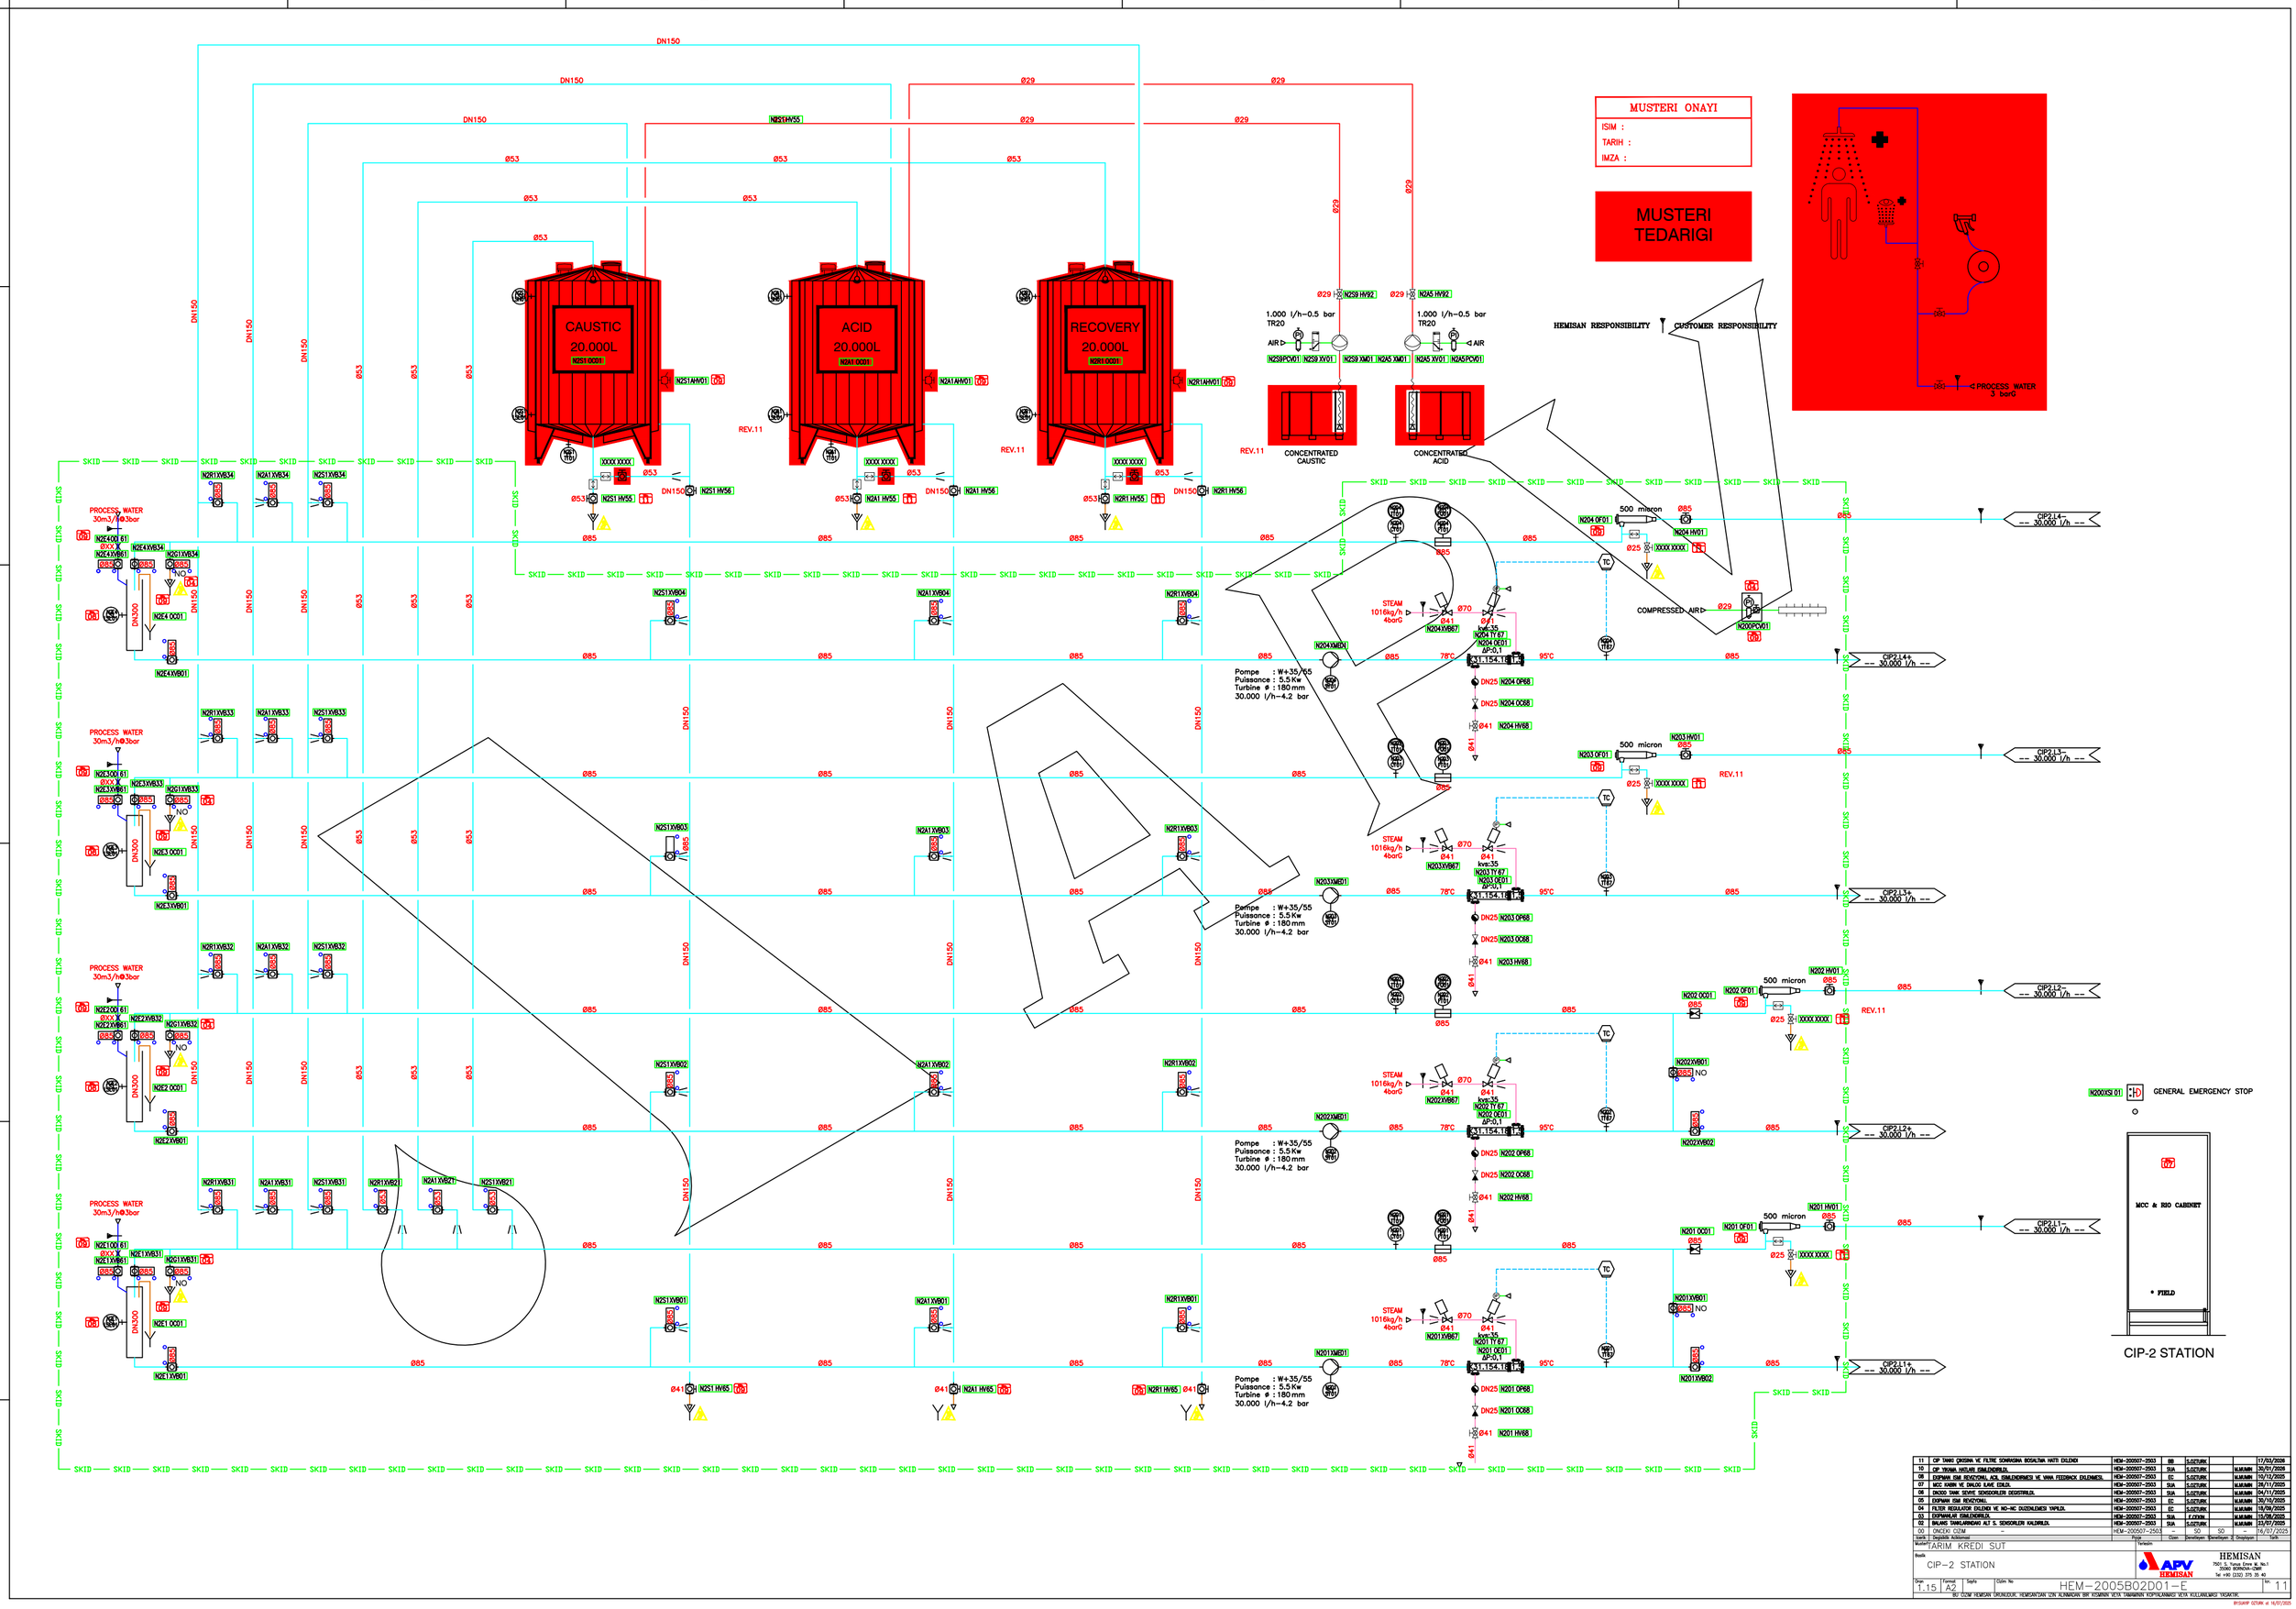

11	CIP TANKI ÇIKISINA VE FİLTRE SONRASINA BOŞALTMA HATTI EKLENDİ	HEM-200507-2503	BB	S.OZTURK			17/03/2026
10	CIP TANKA AKTARLAR EKMLENDİRİLİ.	HEM-200507-2503	SUA	S.OZTURK		M.MUMIN	30/01/2026
08	EKPANİ ISMİ REVİZYONU, AÇIK ISMLENDİRMESİ VE VANA FEEDBACK EKLENMESİ.	HEM-200507-2503	EC	S.OZTURK		M.MUMIN	10/12/2025
07	MCC KABİN VE ONLOG ILAVE EDİLİ.	HEM-200507-2503	SUA	S.OZTURK		M.MUMIN	28/11/2025
06	ÇIKIŞO TANK SEVİYE SENSORLERİ DEĞİŞTİRİLİ.	HEM-200507-2503	SUA	S.OZTURK		M.MUMIN	04/11/2025
05	EKPANİ ISMİ REVİZYONU.	HEM-200507-2503	EC	S.OZTURK		M.MUMIN	30/10/2025
04	FİLTER REGULATOR EKLENDİ VE NO-NC DUZENLEMESİ YAPILDI.	HEM-200507-2503	EC	S.OZTURK		M.MUMIN	18/09/2025
03	EKPANİLAR EKMLENDİRİLİ.	HEM-200507-2503	SUA	F.CEVİN		M.MUMIN	15/08/2025
02	BALANS TANKLARINDAKİ ALT S. SENSORLERİ KALDIRILDI.	HEM-200507-2503	SUA	S.OZTURK		M.MUMIN	23/07/2025
00	ONCEKİ ÇİZİM	HEM-200507-2503	–	SO	SO	–	16/07/2025
Sayfa	Değişiklik Açıklaması	Yapılan	Çizim	Denetleyen	Denetleyen 2	Onaylayan	Tarih

Müşteri: TARIM KREDİ SUT

Tarifsizin: HEMISAN

Bosluk: CIP-2 STATION

APV HEMISAN

Ölçüm: 1.15 | Format: A2 | Sayfa: | Çizim No: HEM-2005B02D01-E | Rev: 11

BU ÇİZİM HEMISAN ÜRÜNLÜĞÜ, HEMISAN'DAN İZİN ALINMADAN BİR KOSMAN VEYA TAMAMANA KOPYALANMASI VEYA KULLANILMASI YASAKTIR.

BYSAMP ÇİZİM 16/07/2025